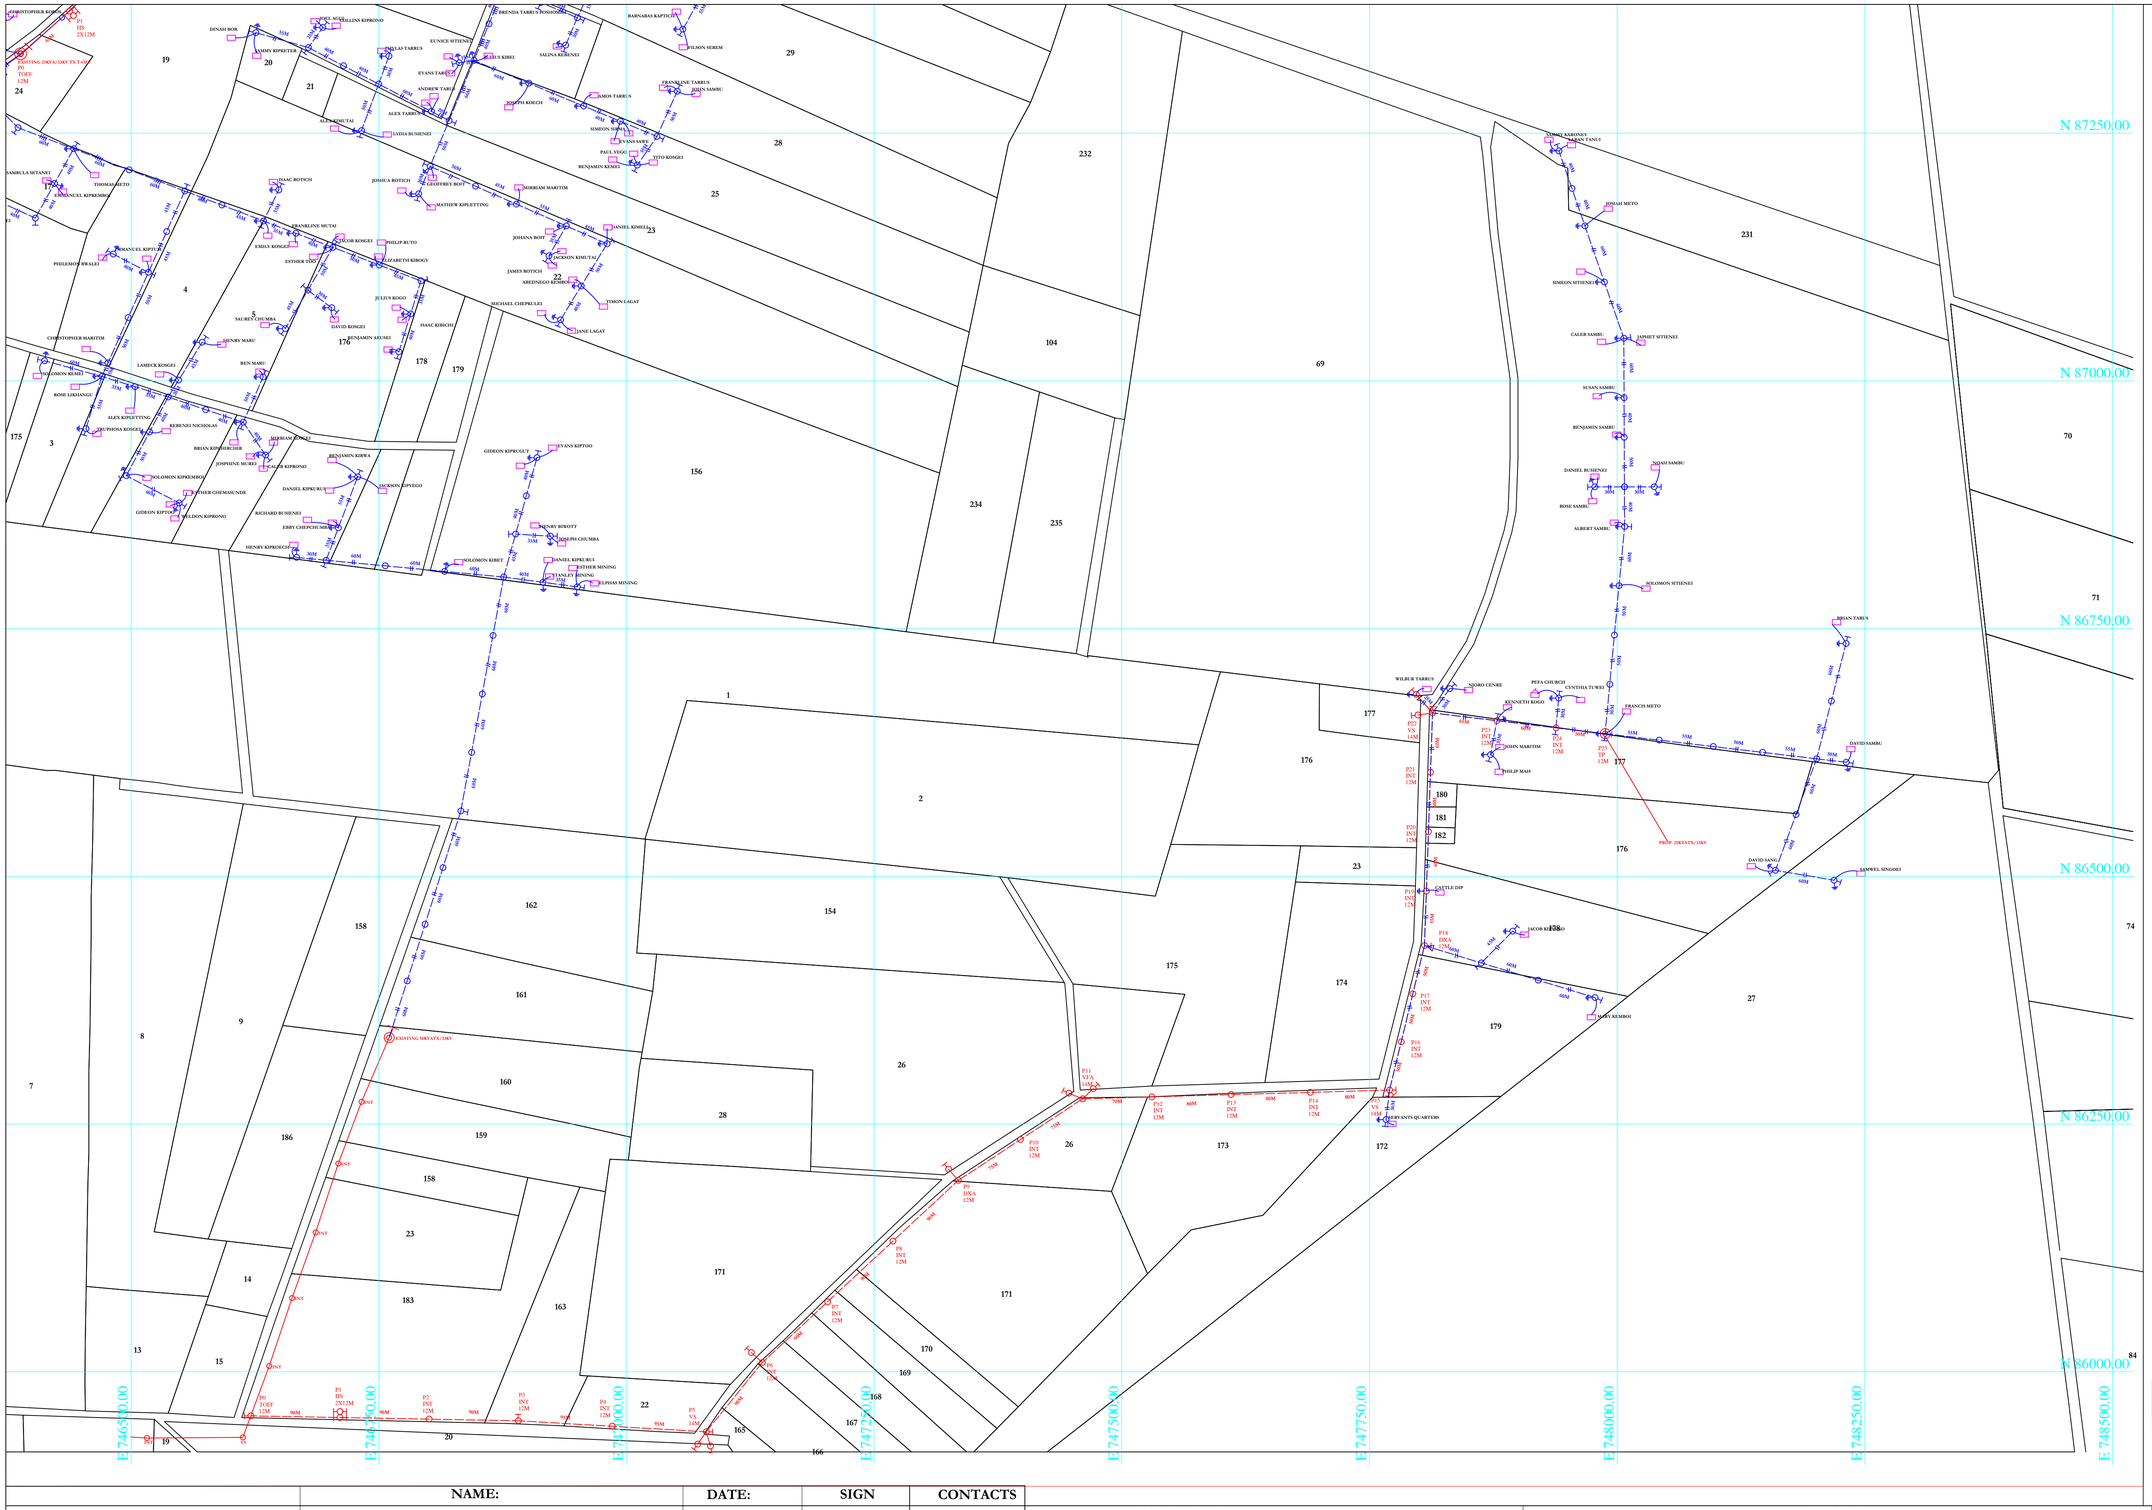

LOCATION DIAGRAM

NOTES

MV & LV O/H LEGEND

- PROPOSED SUB-STATION
- PROPOSED MV POLE
- PROPOSED 11KV MV O/H LINE 75mm2 ACSR Bare Conductor.
- EXISTING MV O/H LINE 75mm2 ACSR Bare Conductor.
- PROPOSED LV O/H LINE 1ph 50mm2 AA HD Bare Conductor
- PROPOSED LV O/H LINE 3ph 50mm2 AA HD Bare Conductor
- PROPOSED 16mm2 SERVICE CABLE
- PROPOSED LV POLE 10M
- EXISTING LV O/H LINE 75mm2 ACSR Bare Conductor.
- HEALTH CENTRE/HOSPITAL
- RELIGIOUS CENTRE
- PUBLIC FACILITY/SCHOOL
- CUSTOMER PREMISE
- ALL WEATHER ROAD
- RIVER
- AIRPORT/AIRFIELD
- RAILWAY LINE
- BRIDGE
- LAND/PARCEL BOUNDARY

COORDINATE SYSTEM AND DATUM:
COORDINATE SYSTEM: Arc 1960 UTM ZONE 36N
PROJECTION : Universal Transverse Mercator
Datum : Arc 1960

NORTH ARROW: N, W, E, S

	NAME:	DATE:	SIGN	CONTACTS
SURVEYED BY:				
CHECKED BY P. SURVEYOR				
DESIGNED BY:	ROSELYNE NAFULA			
CHECKED BY (For) P. ENGINEER:	C.MUTUNE		CWM	
CHECKED BY P. CARTOGRAPHER:				
WAYLEAVES ACQUIRED:				
CHECKED BY P. WAYLEAVES OFFICER:				
APPROVED BY:				

SHEET NUMBER	2 OF 2	PAPER	A1		SCALE	1: 2,500

REVISION (S)

NO	COMMENTS	DATE	SIGN
1			
2			
3			

REF NO: REC-2714125/26004

PROJECT:

NAME; SINENDET VILLAGE.

COUNTY : UASIN GISHU.

CONSTITUENCY : SOY.

CLIENT

REREC
RURAL ELECTRIFICATION AND RENEWABLE ENERGY CORPORATION

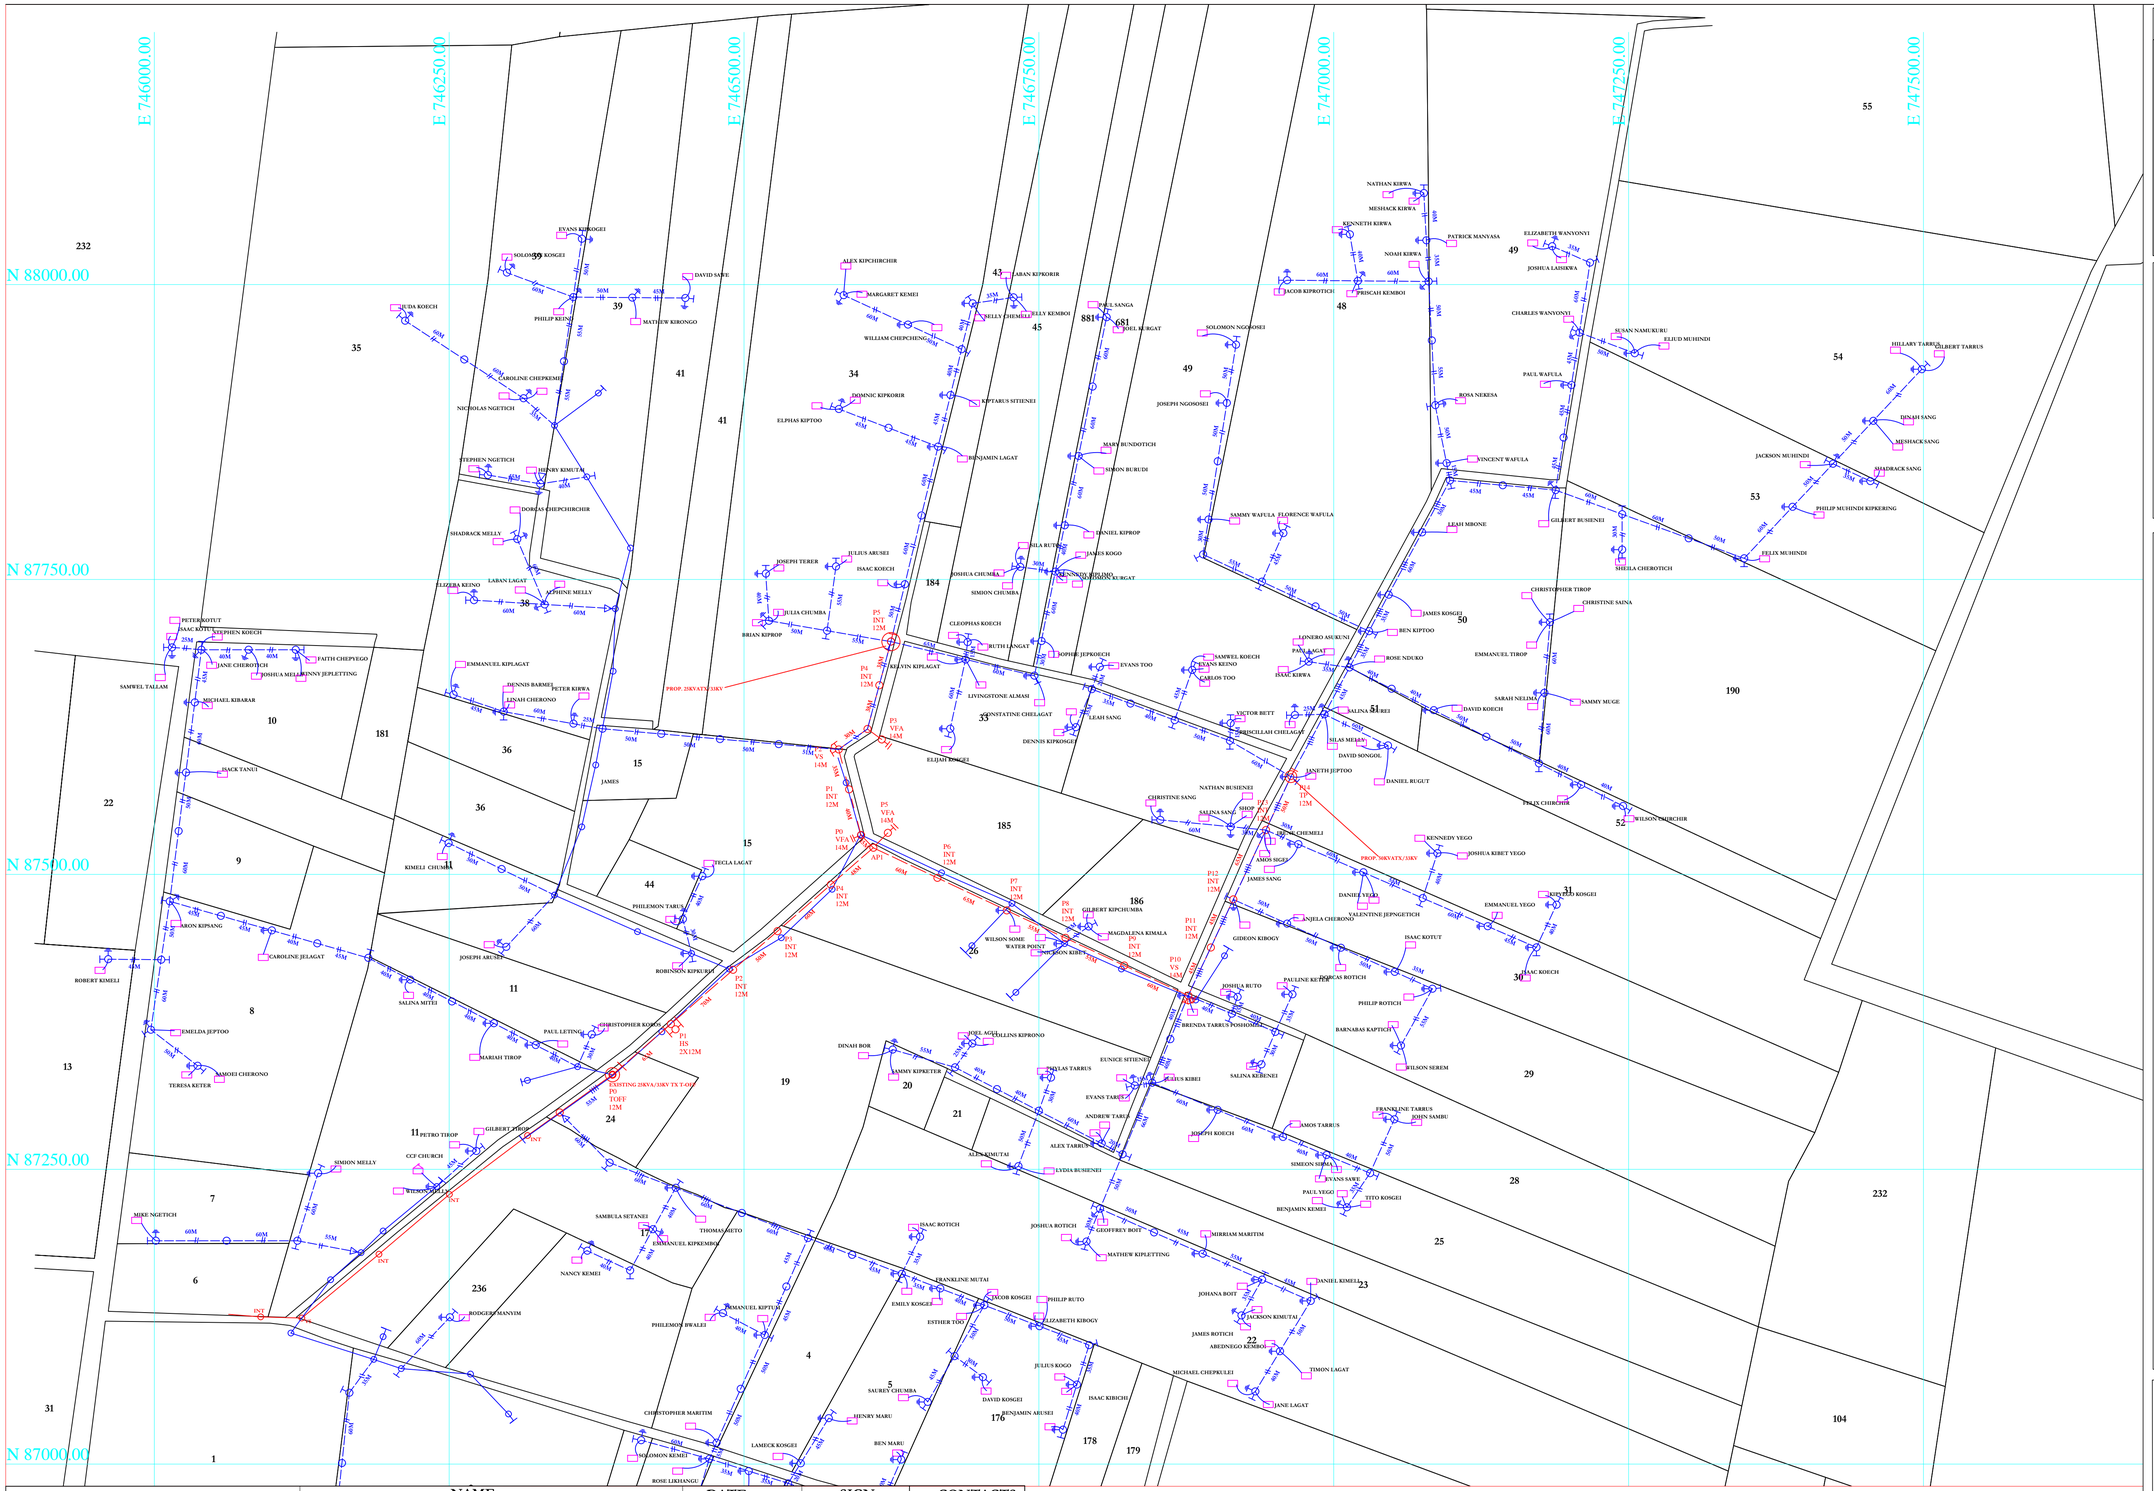

LOCATION DIAGRAM

NOTES

MV & LV O/H LEGEND

- PROPOSED SUB-STATION
- PROPOSED MV POLE
- PROPOSED 11KV MV O/H LINE 75mm2 ACSR Bare Conductor.
- EXISTING MV O/H LINE 75mm2 ACSR Bare Conductor.
- PROPOSED LV O/H LINE 1ph 50mm2 AA HD Bare Conductor
- PROPOSED LV O/H LINE 3ph 50mm2 AA HD Bare Conductor
- PROPOSED 16mm2 SERVICE CABLE
- PROPOSED LV POLE 10M
- EXISTING LV O/H LINE 75mm2 ACSR Bare Conductor.
- HEALTH CENTRE/HOSPITAL
- RELIGIOUS CENTRE
- PUBLIC FACILITY/SCHOOL
- CUSTOMER PREMISE
- ALL WEATHER ROAD
- RIVER
- AIRPORT/AIRFIELD
- RAILWAY LINE
- BRIDGE
- LAND/PARCEL BOUNDARY

COORDINATE SYSTEM AND DATUM:
COORDINATE SYSTEM: Arc 1960 UTM ZONE 36N
PROJECTION : Universal Transverse Mercator
Datum : Arc 1960

NORTH ARROW: N, W, E, S

	NAME:	DATE:	SIGN	CONTACTS
SURVEYED BY:				
CHECKED BY P. SURVEYOR				
DESIGNED BY:	ROSELYNE NAFULA			
CHECKED BY (For) P. ENGINEER:	C.MUTUNE		CWM	
CHECKED BY P. CARTOGRAPHER:				
WAYLEAVES ACQUIRED:				
CHECKED BY P. WAYLEAVES OFFICER:				
APPROVED BY:				

SHEET NUMBER	1 OF 2	PAPER	A1		SCALE	1: 2,500

REVISION (S)

NO	COMMENTS	DATE	SIGN
1			
2			
3			

REF NO: REC-2714125/26004

PROJECT:

NAME; SINENDET VILLAGE.

COUNTY : UASIN GISHU.

CONSTITUENCY : SOY.

CLIENT

REREC
RURAL ELECTRIFICATION AND RENEWABLE ENERGY CORPORATION