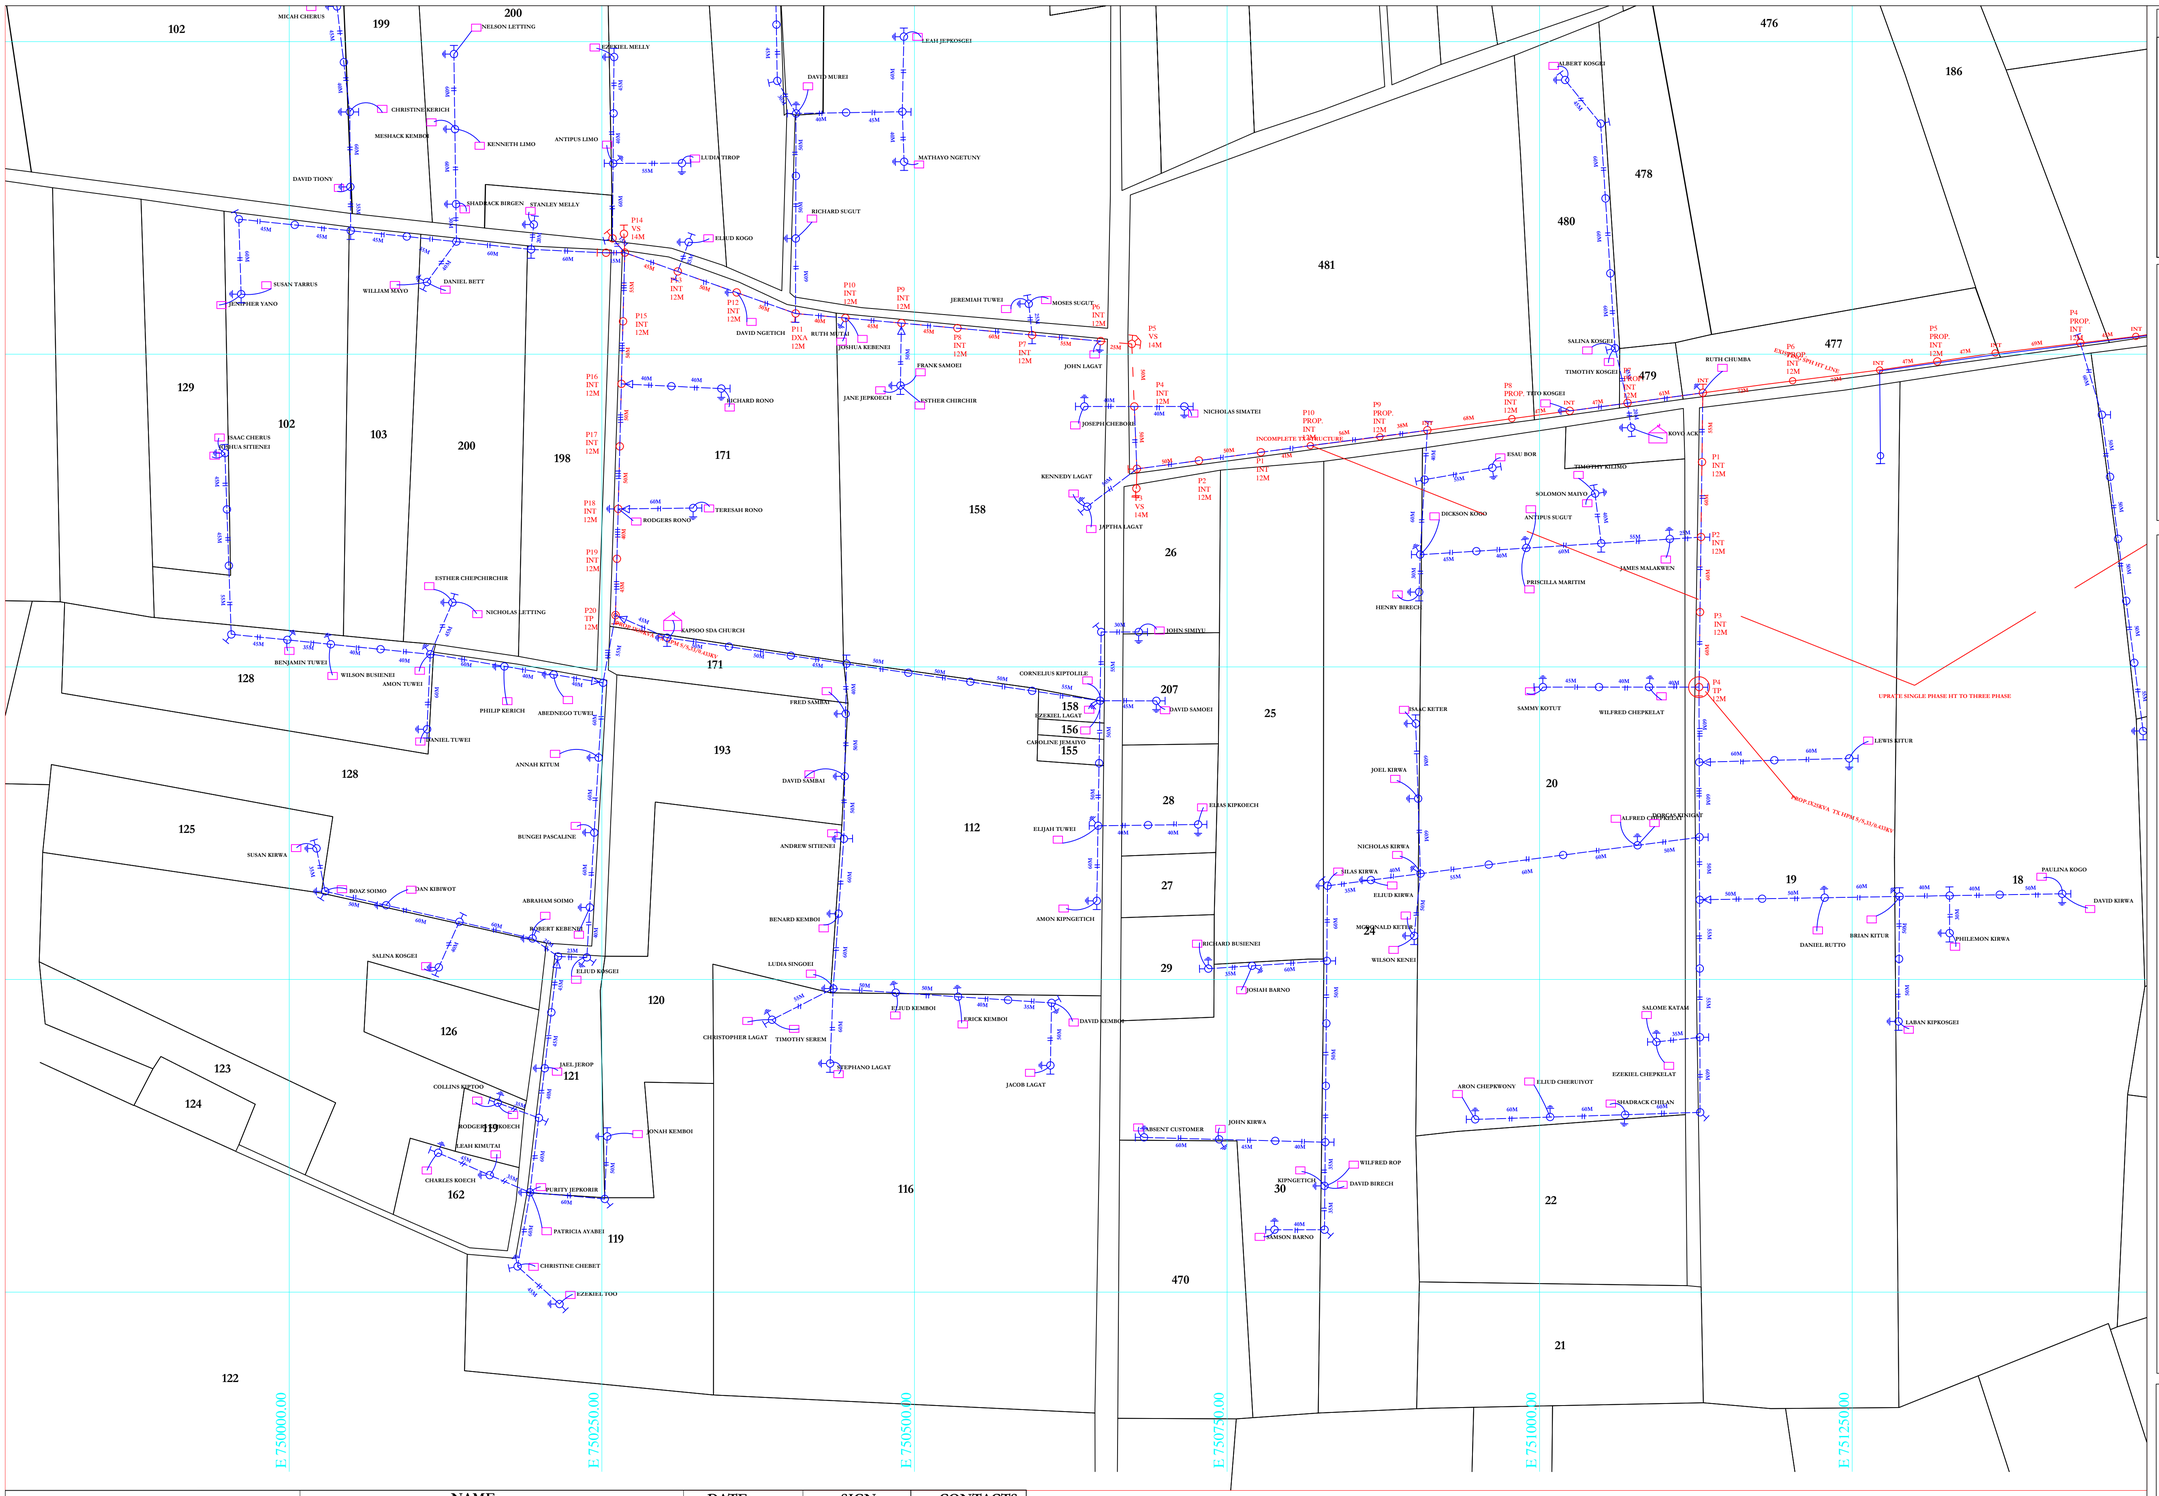

LOCATION DIAGRAM

.\SARAMEK TOPO.jpg

NOTES

MV & LV O/H LEGEND

- PROPOSED SUB-STATION
- PROPOSED MV POLE
- PROPOSED 11KV MV O/H LINE 75mm2 ACSR Bare Conductor.
- EXISTING MV O/H LINE 75mm2 ACSR Bare Conductor.
- PROPOSED LV O/H LINE 1ph 50mm2 AA HD Bare Conductor
- PROPOSED LV O/H LINE 3ph 50mm2 AA HD Bare Conductor
- PROPOSED 16mm2 SERVICE CABLE
- PROPOSED LV POLE 10M
- EXISTING LV O/H LINE 75mm2 ACSR Bare Conductor.
- HEALTH CENTRE/HOSPITAL
- RELIGIOUS CENTRE
- PUBLIC FACILITY/SCHOOL
- CUSTOMER PREMISE
- ALL WEATHER ROAD
- RIVER
- AIRPORT/AIRFIELD
- RAILWAY LINE
- BRIDGE
- LAND/PARCEL BOUNDARY

COORDINATE SYSTEM AND DATUM:

COORDINATE SYSTEM: Arc 1960 UTM ZONE 36N

PROJECTION : Universal Transverse Mercator

Datum : Arc 1960

NORTH ARROW

N W E S

	NAME:	DATE:	SIGN	CONTACTS
SURVEYED BY:	JACINTA PKANIA	JULY/2025		JACINTA.PKANIA@REREC.CO.KE
CHECKED BY P. SURVEYOR				
DESIGNED BY:	ROSELYNE NAFULA			
CHECKED BY P. ENGINEER:				
CHECKED BY P. CARTOGRAPHER:				
WAYLEAVES ACQUIRED:				
CHECKED BY P. WAYLEAVES OFFICER:				
APPROVED BY:				

REVISION (S)

NO	COMMENTS	DATE	SIGN
1			
2			
3			

REF NO:REC-2714124/25057

PROJECT:

NAME; SARAMEK.

COUNTY : UASIN GISHU.

CONSTITUENCY : SOY.

CLIENT

REREC

RURAL ELECTRIFICATION AND RENEWABLE ENERGY CORPORATION

C:\Users\dunnm\Downloads\SARAMEK.dwg-1.dwg-1.dwg, 11/5/2025 12:33:04 PM, DWG To PDF.pc3